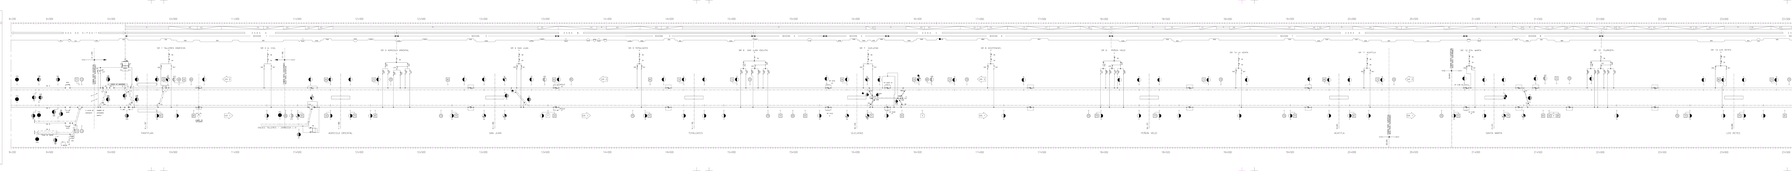

S.T.C METRO

LINEA A

**PLANO DE PERFIL ,
SEÑALIZACION Y
ALIMENTACION - TRACCION**

PANTITLAN - LA PAZ

**DIRECCIÓN DE INGENIERÍA
Y DESARROLLO TECNOLÓGICO**

**GERENCIA DE INGENIERÍA Y
NUEVOS PROYECTOS**

**COORDINACIÓN DE DESARROLLO
TECNOLÓGICO**

ESC: 1 : 5000

AREA DE DIFUSION Y ACTUALIZACION TECNOLOGICA
ABRIL 2004 Vazquez Hernández Felipe de Jesus.

No.	MODIFICACIONES	FECHA	APROBO
△			

SIMBOLOGIA

- SECCIONADOR INVERSOR BIPOLAR MANUAL
- INTERRUPTOR AUTOMATICO
- SECCIONADOR MANUAL
- SECCIONADOR INVERSOR MANUAL
- N POSICION NORMAL
- S POSICION SOCORRO
- LM PLACA DE LIMITE DE MANIOBRA
- J24A/44A JOA SEÑALES 24A y 44A
- SEÑAL FIJA DE ALTO
- SEÑAL DE 2 LUCES
- SEÑAL DE 3 LUCES
- SEÑAL DE 4 LUCES
- SEÑAL CON INDICACION DE DIRECCION
- ROJO
- AMARILLO
- VERDE
- ADVERTIDOR DE I L V
- EJECUTOR DE ILV
- RECUPERADOR DE I L V
- RECUPERADOR DE I V A
- (22) CIRCUITO DE VIA o CDV 22
- ZONA DE VISIBILIDAD REDUCIDA
- CC PLACA CAMBIO DE CABINA

SIMBOLOGIA

- CORTE NO PUENTEABLE
- CC RECUPERADOR DE I V A
- INTERRUPTOR AUTOMATICO
- INTERRUPTOR DE AISLAMIENTO TELEMANDO DE ACCIONAMIENTO SIMULTANEO PARA IAT
- SECCIONADOR DE FOSA DE VISITA
- AISLAMIENTO EN AIRE
- INTERRUPTOR DE VIA DE ENLACE
- SECCIONAMIENTO MECANICO

CTP	CONTACTOR DE TRAMO DE PROTECCION
DV	DISYUNTOR DE VIA
DVS	DISYUNTOR DE VIA SECUNDARIA
IAT	INTERRUPTOR DE AISLAMIENTO TELEMANDO
IAZ	INTERRUPTOR DE AISLAMIENTO TELEMANDO VIA Z
IZ	INTERRUPTOR INVERSOR VIA Z
IT	INTERRUPTOR DE TERMINAL TELEMANDO

9+200
9+500
10+000
10+500
11+000
11+500
12+000
12+500
13+000
13+500
14+000
14+500
15+000
15+500
16+000
16+500
17+000
17+500
18+000
18+500
19+000
19+500
20+000
20+500
21+000
21+500
22+000
22+500
23+000
23+500
24+000
24+500
25+000
25+500
26+000
26+500
ZONA DE DIPOSITO
ZONA A
SECCION 1
SECCION 2
ZONA B
SECCION 3
SECCION 4
SECCION 5
ZONA C
SECCION 6
SECCION 7
ZONA D
SECCION 8
SECCION 9
ZONA E
SECCION VIAS SECUNDARIAS
SR 1 TALLERES GRAFICOS
SR 2 A. CIVIL
SR 3 AGRICOLA ORIENTAL
SR 4 SAN JUAN
SR 5 TEPALCATES
SR 6 SAN JUAN ESCUTIA
SR 7 GUELATAO
SR 8 XICOTENCATL
SR 9 PEÑON VIEJO
SR 10 LA VENTA
SR 11 ACATITLA
SR 12 STA. MARTA
SR 13 FLORESTA
SR 14 LOS REYES
SR 15 H. ILUSTRES
SR 16 LA PAZ
VIA 1
VIA 2
VIA A
VIA B
VIA C
VIA D
VIA L
A TALLERES LA PAZ
ANDEN DE MANIOBRAS
FOSA DE VISITA
CAMBIO DE CATENARIA
ENLACE TALLERES - ZARAGOZA L-A
PANTITLAN
AGRICOLA ORIENTAL
SAN JUAN
TEPALCATES
GUELATAO
PEÑON VIEJO
ACATITLA
SANTA MARTA
LOS REYES
LA PAZ
CADENAMIENTO TOPE DE FIN DE VIA 26 + 416