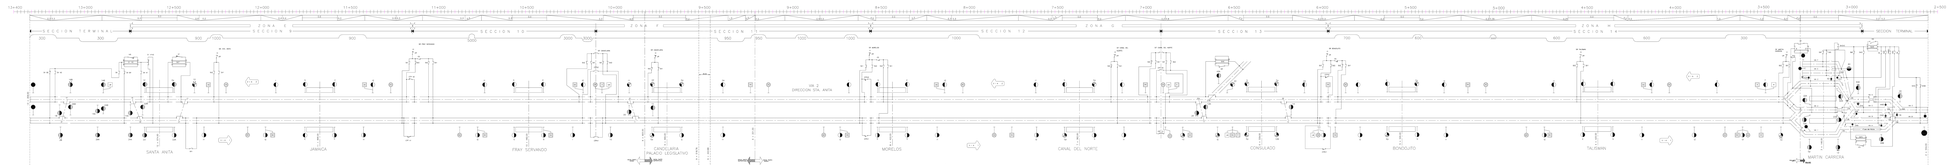

S.T.C
METRO

LINEA 4

PLANO DE PERFIL ,
SEÑALIZACION Y
ALIMENTACION - TRACCION

SANTA ANITA - MARTIN CARRERA

DIRECCIÓN DE INGENIERÍA
Y DESARROLLO TECNOLÓGICO

GERENCIA DE INGENIERÍA Y
NUEVOS PROYECTOS

COORDINACIÓN DE DESARROLLO
TECNOLÓGICO

ESC: 1 : 5000

AREA DE DIFUSION Y ACTUALIZACION TECNOLOGICA
JULIO 2004

No.	MODIFICACIONES	FECHA	APROBO
⚠	- A LA FECHA DE ELABORACION DEL PLANO LAS SEÑALES " Ep " DE MARTIN CARRERA NO TENIAN PLACA DE IDENTIFICACION DE VIA		

SIMBOLOGIA

N SIB N / S S	SECCIONADOR INVERSOR BIPOLAR MANUAL
	INTERRUPTOR AUTOMATICO
	SECCIONADOR MANUAL
S N	SECCIONADOR INVERSOR MANUAL
N	POSICION NORMAL
S	POSICION SOCORRO
LM	PLACA DE LIMITE DE MANIOBRA
J24A/44A	JDA SEÑALES 24A y 44A
●	SEÑAL FIJA DE ALTO
	SEÑAL DE 2 LUCES
	SEÑAL DE 3 LUCES
	SEÑAL DE 4 LUCES
o° o	SEÑAL CON INDICACION DE DIRECCION
	ROJO
	AMARILLO
	VERDE
40	ADVERTIDOR DE I L V
40	EJECUTOR DE ILV
R	RECUPERADOR DE I L V
R	RECUPERADOR DE I V A
(22)	CIRCUITO DE VIA o CDV 22
	ZONA DE VISIBILIDAD REDUCIDA
CC	PLACA CAMBIO DE CABINA

13+400
13+000
12+500
12+000
11+500
11+000
10+500
10+000
9+500
9+000
8+500
8+000
7+500
7+000
6+500
6+000
5+500
5+000
4+500
4+000
3+500
3+000
2+500
ZONA E
ZONA F
ZONA G
ZONA H
SECCION TERMINAL
SECCION 9
SECCION 10
SECCION 11
SECCION 12
SECCION 13
SECCION 14
SECCION TERMINAL
SR STA. ANITA
SR FRAY SERVANDO
SIT CANDELARIA
SR CANDELARIA
SR MORELOS
SR CANAL DEL NORTE
SIT CANAL DEL NORTE
SR BONDOJITO
SR TALISMAN
SR MARTIN CARRERA
VIA 2
VIA 1
VIA 2
DIRECCION STA. ANITA
SANTA ANITA
JAMAICA
FRAY SERVANDO
CANDELARIA
PALACIO LEGISLATIVO
MORELOS
CANAL DEL NORTE
CONSULADO
BONDOJITO
TALISMAN
MARTIN CARRERA