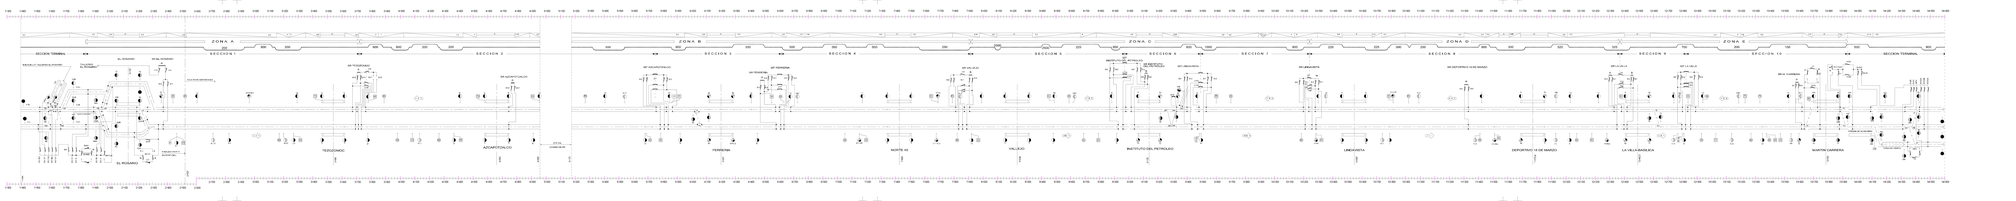

S.T.C
METRO

LINEA 6

PLANO DE PERFIL,
SEÑALIZACION Y
ALIMENTACION - TRACCION

EL ROSARIO - MARTIN CARRERA

DIRECCIÓN DE INGENIERÍA
Y DESARROLLO TECNOLÓGICO

GERENCIA DE INGENIERÍA Y
NUEVOS PROYECTOS

COORDINACIÓN DE DESARROLLO
TECNOLÓGICO

ESC: 1 : 5000

AREA DE DIFUSION Y ACTUALIZACION TECNOLOGICA
ABRIL 2004 Vázquez Hernández Felipe de Jesús.

No.	MODIFICACIONES	FECHA	APROBO
△	• Se modifica :		

SIMBOLOGIA

- SECCIONADOR INVERSOR BIPOLAR MANUAL
- INTERRUPTOR AUTOMATICO
- SECCIONADOR MANUAL
- SECCIONADOR INVERSOR MANUAL
- N — POSICION NORMAL
- S — POSICION SOCORRO
- LM — PLACA DE LIMITE DE MANIOBRA
- J24A/44A — JDA SEÑALES 24A y 44A
- SEÑAL FIJA DE ALTO
- SEÑAL DE 2 LUCES
- SEÑAL DE 3 LUCES
- SEÑAL DE 4 LUCES
- SEÑAL CON INDICACION DE DIRECCION
- ROJO
- AMARILLO
- VERDE
- ADVERTIDOR DE I.L.V
- EJECUTOR DE ILV
- R — RECUPERADOR DE I L V
- R — RECUPERADOR DE I V A
- 22 — CIRCUITO DE VIA o CDV 22
- ZONA DE VISIBILIDAD REDUCIDA
- CC — PLACA CAMBIO DE CABINA

ZONA A
ZONA B
ZONA C
ZONA D
ZONA E
SECCION TERMINAL
SECCION 1
SECCION 2
SECCION 3
SECCION 4
SECCION 5
SECCION 6
SECCION 7
SECCION 8
SECCION 9
SECCION 10
SECCION TERMINAL
ENLACE L-6 TALLERES EL ROSARIO
TALLERES EL ROSARIO
EL ROSARIO
SR EL ROSARIO
INICIA PARTE SUBTERRANEA
FINALIZA PARTE SUPERFICIAL
SR TEZOZOMOC
SR AZCAPOTZALCO
SIT AZCAPOTZALCO
SR FERRERIA
SIT FERRERIA
SR VALLEJO
SIT INSTITUTO DEL PETROLEO
SR INSTITUTO DEL PETROLEO
SIT LINDAVISTA
SR LINDAVISTA
SR DEPORTIVO 18 DE MARZO
SR LA VILLA
SIT LA VILLA
SR M. CARRERA
EL ROSARIO
TEZOZOMOC
AZCAPOTZALCO
216 mts.
CAMBIO DE PK
FERRERIA
NORTE 45
VALLEJO
INSTITUTO DEL PETROLEO
LINDAVISTA
DEPORTIVO 18 DE MARZO
LA VILLA-BASILICA
MARTIN CARRERA
ANDEN DE MANIOBRA
FOSA DE VISITA
VIA 1
VIA 2
1+300
14+600